


FLOOR PLAN


SCALE 1:24 | 1/2 IN = 1 FT | PRINT AT 100%

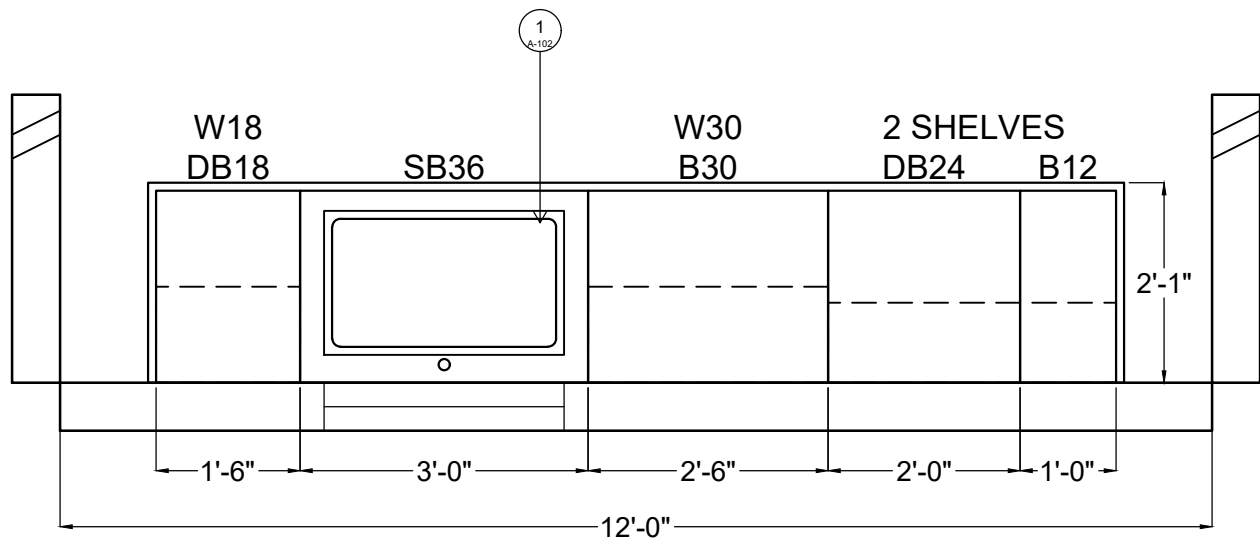

FINISH: PAINTED EXCEPT B30 + SHELVES = STAINED OAK | GRAIN PER A-102

FRONT ELEVATION

SCALE 1:24 | 1/2 IN = 1 FT

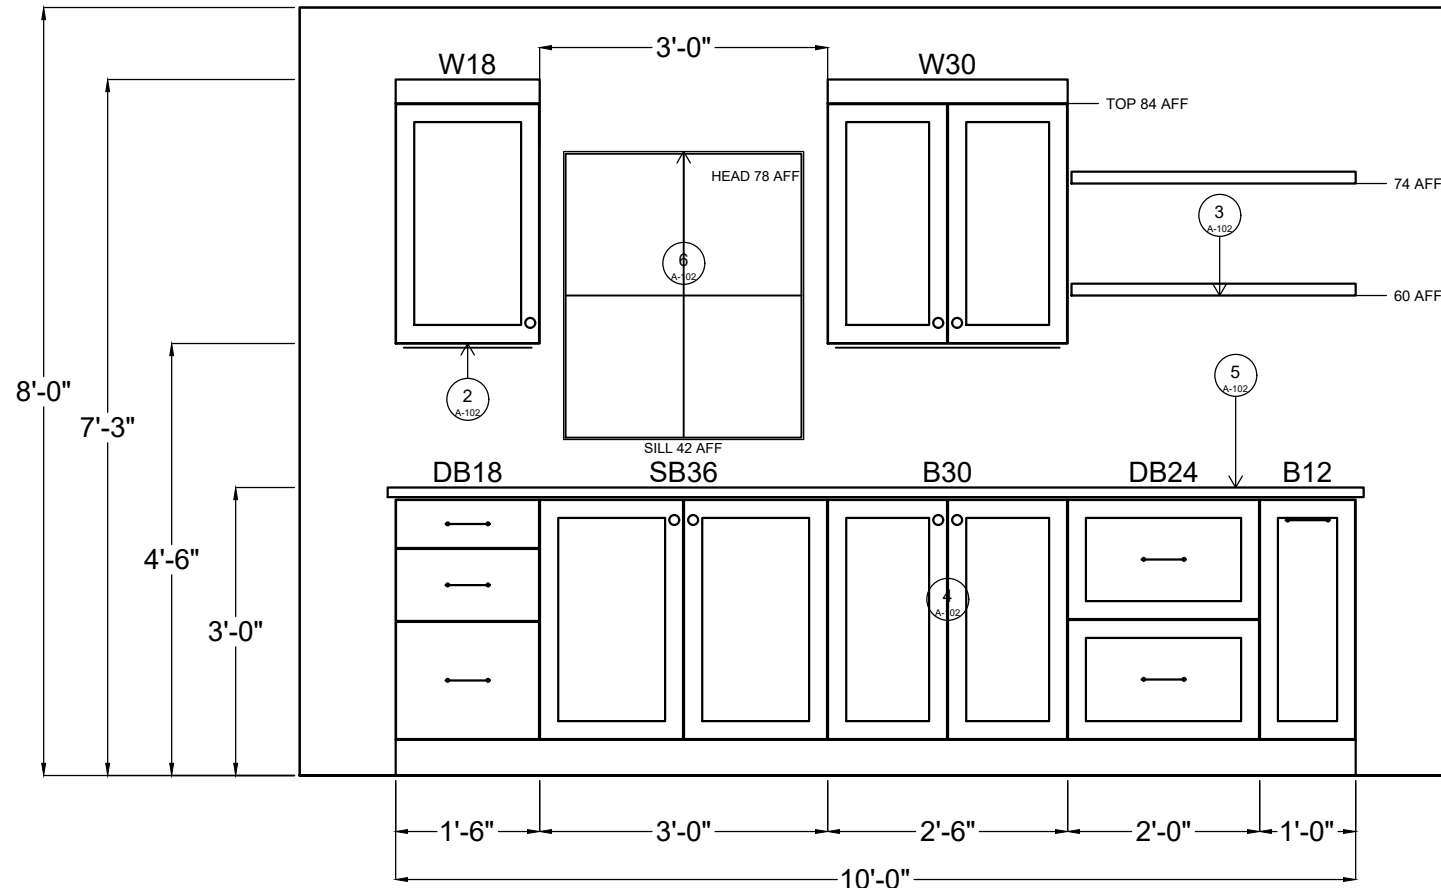

DESIGN AND MATERIAL NOTES

- BASIS PRODUCTS SHOWN; VERIFY DATA AND FIELD CONDITIONS.
- PAINT: BM ADVANCE, PRECIOUS IVORY 185, SATIN (LRV 70.38).
- B30/SHELVES: RIFT-SAWN WHITE OAK; GF ANTIQUE OAK STAIN + CLEAR SATIN TOPCOAT, WATER-BASED (TBD/UNPRICED IF GENERIC).
- CAMBRIA EVERLEIGH WARM, MATTE, 3 CM; TOP = 36 IN AFF.
- SR3018 SINK CUTOUT/REVEAL PER PURCHASED TEMPLATE.
- FIVE-PIECE FRONTS: 1/8 IN GAPS; 2-1/4 IN STILES/RAILS.
- PULLS: BP36853CZ, 128 MM C-C; KNOBS: BP55342CZ; CHAMPAGNE BRONZE.
- NO UNDER-CABINET LIGHTING; DAYLIGHT THROUGH WINDOW ONLY (R09).

BASIS-OF-DESIGN PRODUCT KEYS

- P-01 NANTUCKET SR3018 SINK, 30x18x10
P-02 DELTA 9159-CZ-DST FAUCET
P-03 CAMBRIA EVERLEIGH WARM, 3 CM
P-04 ANDERSEN 100, 2630; UNIT 29-1/2x35-1/2; RO 30x36
D-01 AMEROCK BP36853CZ, QTY 6
D-02 AMEROCK BP55342CZ, QTY 7
H-01 BLUM 71B3550 + 173H7100, QTY 14
H-03 BLUM 563H5330B + T51, QTY 5 PAIR
H-05 REV-A-SHELF 448UT-BCSC-8C
H-06 HOVR 18 IN; SHELF BOTTOMS 60 / 74 AFF

CABINET ABBREVIATIONS

- DB = DRAWER BASE CABINET
SB = SINK BASE CABINET
B = BASE CABINET
W = WALL CABINET
NUMBER = NOMINAL WIDTH IN INCHES
DB18 / DB24 = 18 / 24 IN DRAWER BASE
SB36 = 36 IN SINK BASE
B30 / B12 = 30 / 12 IN BASE
W18 / W30 = 18 / 30 IN WALL CABINET
AFF = ABOVE FINISHED FLOOR; C-C = CENTER TO CENTER

WARM TRANSITIONAL CUSTOM KITCHEN

A-101 | PLAN AND FRONT ELEVATION

SAMUEL BROWN | INDEPENDENT CAD PORTFOLIO STUDY
DATE: SEPTEMBER 2026